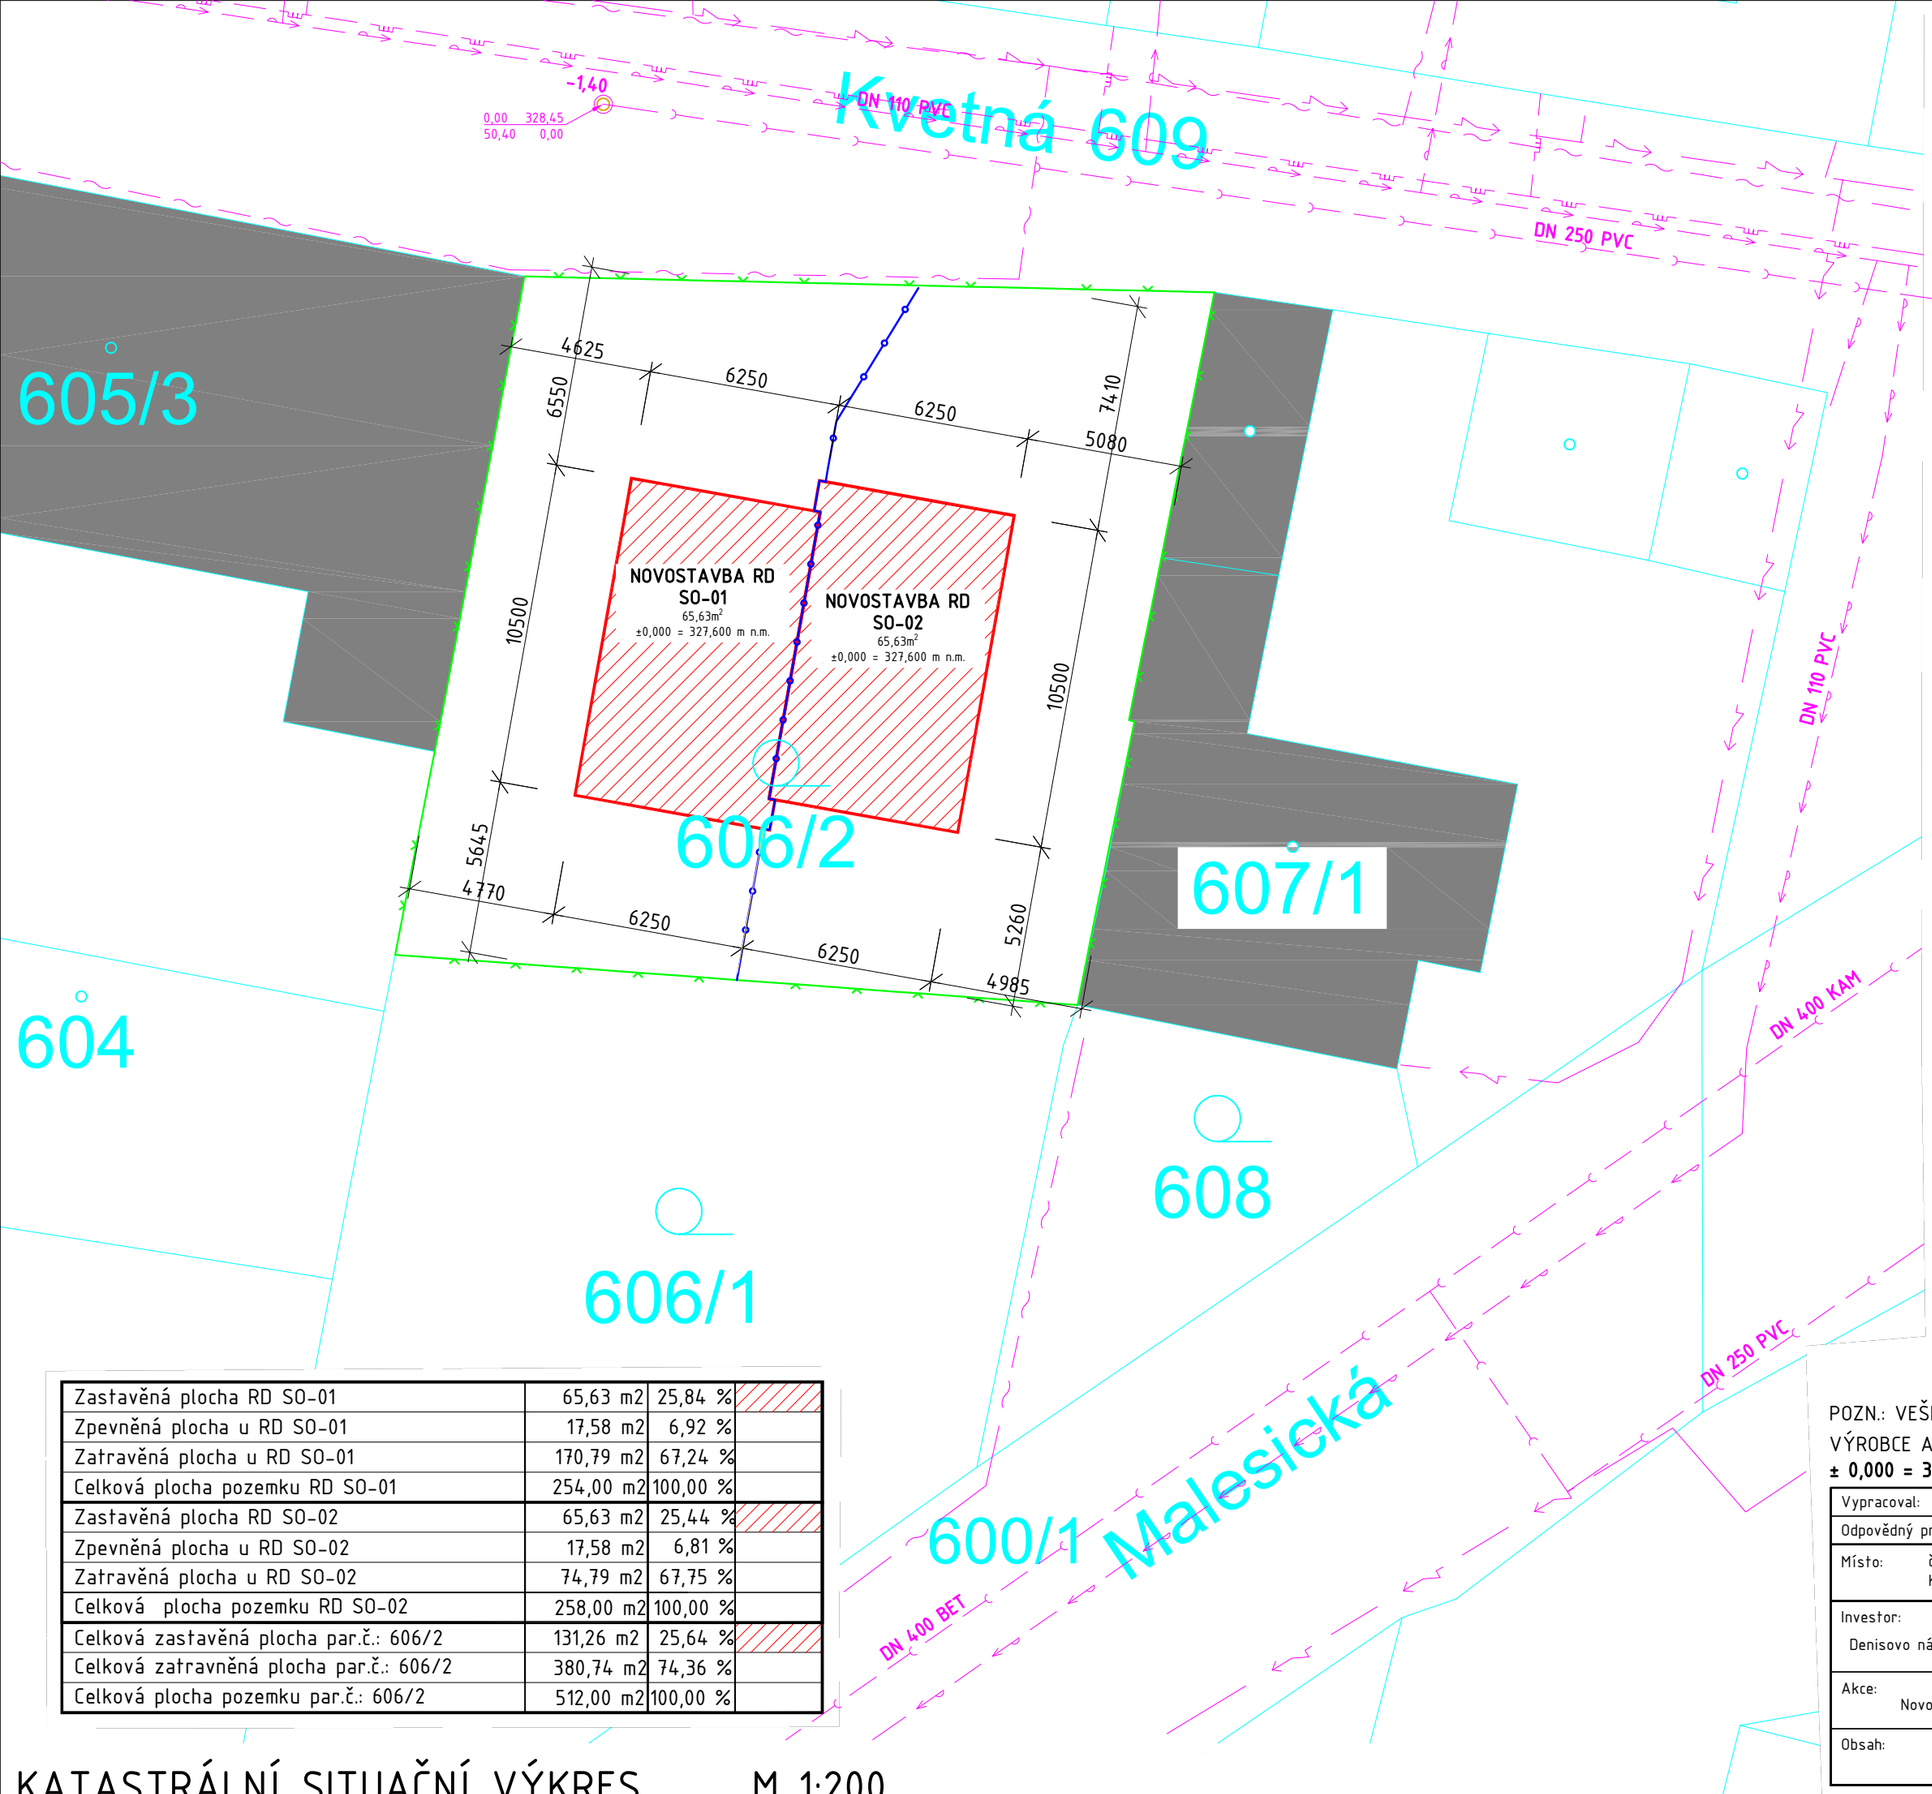


LEGENDA SITUACE:

- NOVOSTAVBA ŘADOVÉHO RODINNÉHO DOMU
- Stávající objekty z KN
- Hranice dotčeného území par.č.: 606/2
- Navrhovaná hranice dělení pozemku par.č.: 606/2
- Hranice parcel z katastru nemovitostí

Parcelní čísla sousedních pozemků:
č. par.: 605/3, 606/1, 607/1, 608, 609

Zastavěná plocha RD SO-01	65,63 m2	25,84 %	
Zpevněná plocha u RD SO-01	17,58 m2	6,92 %	
Zatravěná plocha u RD SO-01	170,79 m2	67,24 %	
Celková plocha pozemku RD SO-01	254,00 m2	100,00 %	
Zastavěná plocha RD SO-02	65,63 m2	25,44 %	
Zpevněná plocha u RD SO-02	17,58 m2	6,81 %	
Zatravěná plocha u RD SO-02	74,79 m2	67,75 %	
Celková plocha pozemku RD SO-02	258,00 m2	100,00 %	
Celková zastavěná plocha par.č.: 606/2	131,26 m2	25,64 %	
Celková zatravněná plocha par.č.: 606/2	380,74 m2	74,36 %	
Celková plocha pozemku par.č.: 606/2	512,00 m2	100,00 %	

Podepsal Ing. Tomáš Lohr
DN: cn=Ing. Tomáš Lohr, c=CZ, o=Česká komora autorizovaných inženýrů a techniků činných ve výstavbě, ou=0202496, email=lohrtomas@seznam.cz
Datum: 2025.11.03 22:40:35 +01'00'

POZN.: VEŠKERÉ KONSTRUKCE PROVÁDĚT DLE TECHNOLOGICKÝCH DOPORUČENÍ VÝROBCE A PŘÍSLUŠNÝCH NOREM

± 0,000 = 327,600 m n.m. Souřadnicový systém JTSK, Výškový systém B.p.v.

Vypracoval: Ing. Tomáš Lohr		Adresa: Klatovská třída 1460/83, 301 00 Plzeň	
Odpovědný projektant: Ing. Tomáš Lohr			
Místo: č.p. 606/2; Obec: Město Touškov [559211] Katastrální území: Město Touškov [693430]			
Investor: Ostreto s.r.o., Denisovo nábřeží 2568/6, Východní Předměstí, 30100 Plzeň		Zakázka:	Měřítko: 1:200
		Formát: 2xA4	Datum: 09/2025
Akce: Novostavba řadového rodinného domu - dvojdům		Stupeň: DSP	Paré:
Obsah: KATASTRÁLNNÍ SITUAČNÍ VÝKRES		Č. výkresu: C.2	

KATASTRÁLNÍ SITUAČNÍ VÝKRES M 1:200