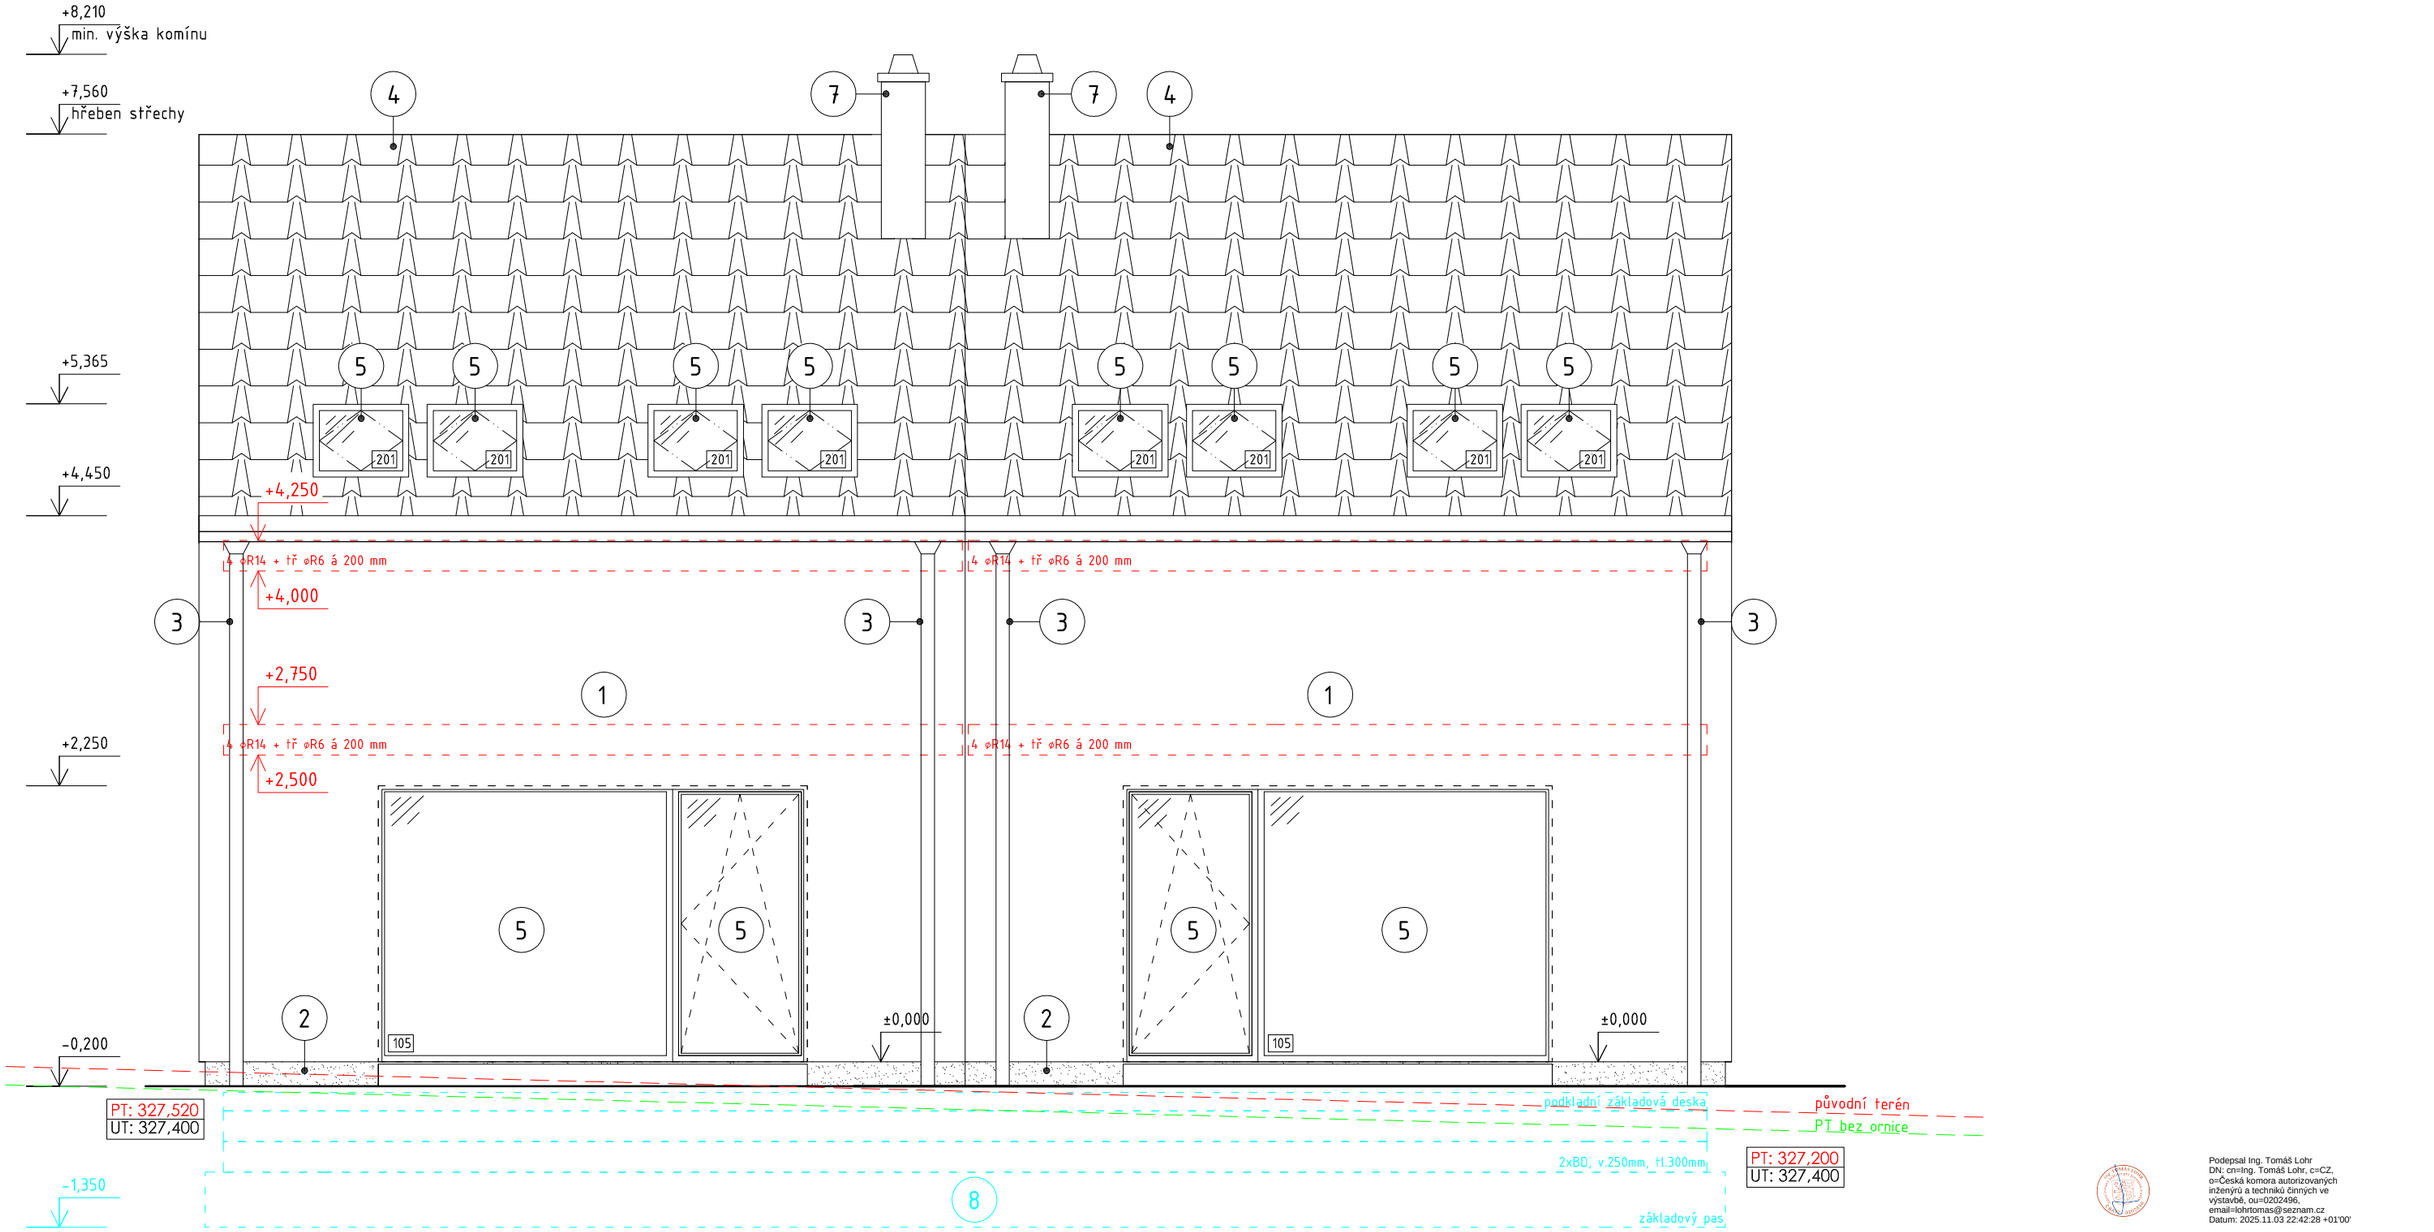


Podepsal Ing. Tomáš Lohr
DN: cn=Ing. Tomáš Lohr, c=CZ, o=Česká komora autorizovaných inženýrů a techniků činných ve výstavbě, ou=0202496, email=lohrtomas@seznam.cz
Datum: 2025.11.03 22:42:28 +01'00'

LEGENDA KONSTRUKCÍ:

1. OMÍTKA ŠTUKOVÁ JEMNÁ - BARVA BÍLÁ
2. SOKL - OMÍTKA HRUBOZRNNÁ
3. KLEMPÍŘSKÉ PRVKY, BAREVNÝ POZINK
4. ZASTŘEŠENÍ - STŘEŠNÍ KRYTINA BRAMAC
5. VÝPLŇOVÉ PRVKY OKNA/DVEŘE (RD - IZOLAČNÍ 3-SKLA)
6. VĚTRACÍ HLAVICE
7. KOMÍNOVÉ TĚLESO NAPŘ.: SCHIEDEL ABSOLUT
8. KONSTRUKCE PLOŠNÉHO ZALOŽENÍ - ZÁKLADOVÉ PASY

POHLED JIŽNÍ M 1:50

POZN.: VEŠKERÉ KONSTRUKCE PROVÁDĚT DLE TECHNOLOGICKÝCH DOPORUČENÍ VÝROBCE A PŘÍSLUŠNÝCH NOREM

± 0,000 = 327,600 m n.m. Souřadnicový systém JTSK, Výškový systém B.p.v.

Vypracoval: Ing. Tomáš Lohr		Adresa: Klatovská třída 1460/83, 301 00 Plzeň	
Odpovědný projektant: Ing. Tomáš Lohr			
Místo: č.p. 606/2; Obec: Město Touškov [559211] Katastrální území: Město Touškov [693430]			
Investor: Ostreto s.r.o., Denisovo nábřeží 2568/6, Východní Předměstí, 30100 Plzeň		Zakázka:	Měřítko: 1:50
		Formát: 2xA4	Datum: 09/2025
Akce: Novostavba řadového rodinného domu - dvojdům		Stupeň: DSP	Paré:
Obsah: POHLED JIŽNÍ		Č. výkresu: 9	