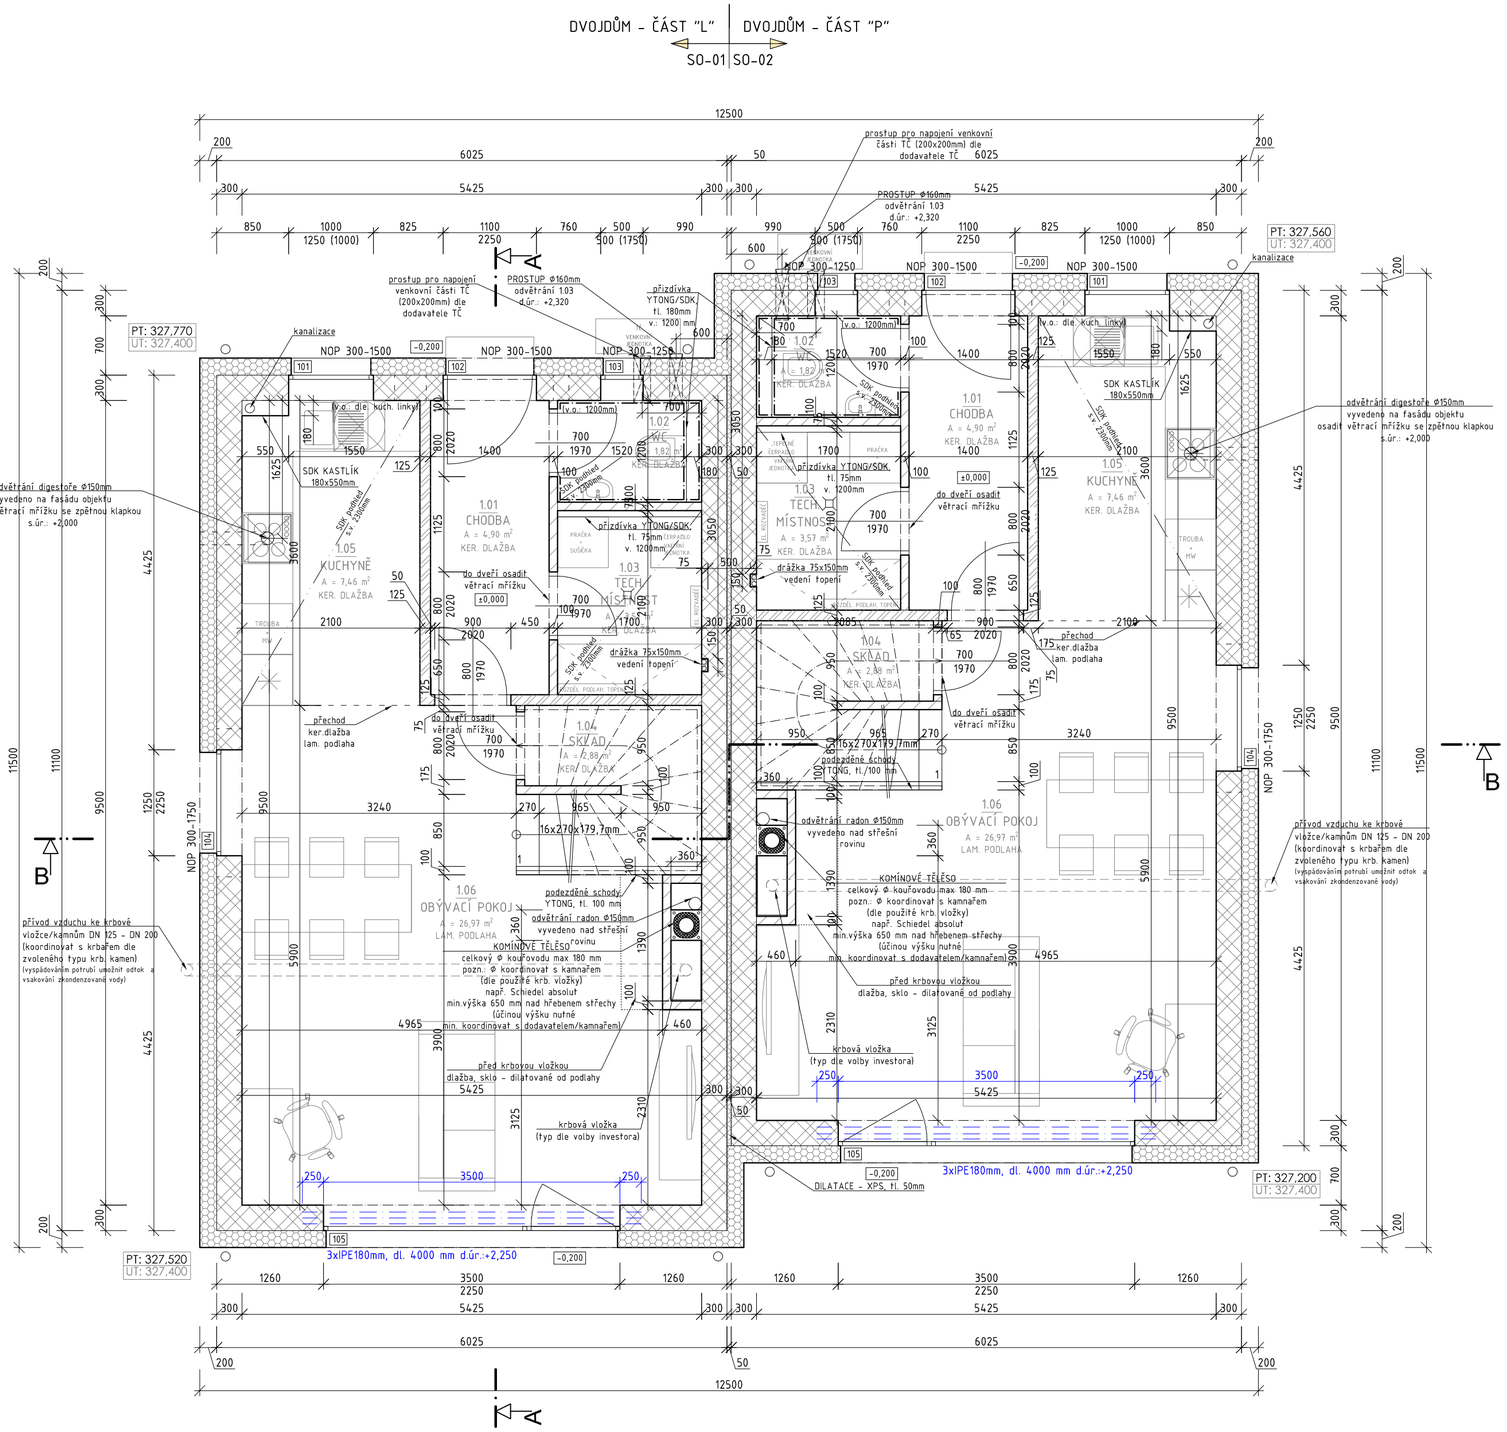


LEGENDA MATERIÁLŮ:

- ZDIVO YTONG STATIK P4-550 PDK, tl. 300 mm (499x300x249mm), NA YTONG TENKOVRSTVÉ MALTOVÉ LOŽE + POLYSTYREN EPS 70 F, tl. 200 mm
- ZDIVO YTONG, tl. 125 mm (599x249x125mm), NA YTONG TENKOVRSTVÉ LEPIDLO
- ZDIVO YTONG, tl. 100 mm (599x249x100mm), NA YTONG TENKOVRSTVÉ LEPIDLO
- INSTALAČNÍ PŘIZDÍVKA, YTONG/SDK, tl. 75-180mm

LEGENDA MÍSTNOSTÍ:

HLAVNÍ OBJEKT - RODINNÝ DŮM:

č.m.	Účel místnosti	Plocha [m²]	Povrchová úprava			Poznámka
			Podlaha	Stěny	Strop	
1.01	CHODBA	4,90	Keramická dlažba	Sádrová omítka +malba	SDK podhled +malba	s.v.: 2500 mm
1.02	WC	1,82	Keramická dlažba	Keramický obklad v. 1200 mm	SDK podhled - zel. +malba	s.v.: 2300 mm
1.03	TECH. MÍSTNOST	3,57	Keramická dlažba	Sádrová omítka +malba	SDK podhled +malba	s.v.: 2300 mm
1.04	SKLAD	2,88	Keramická dlažba	Sádrová omítka +malba	SDK podhled +malba	s.v.: - mm
1.05	KUCHYNĚ	7,46	Keramická dlažba	Sádrová omítka +malba	SDK podhled +malba	s.v.: 2300 mm
1.06	OBÝVACÍ POKOJ + KK	26,97	Laminátová podlaha	Sádrová omítka +malba	SDK podhled +malba	s.v.: 2500 mm
UŽITNÁ PLOCHA SO-01:		47,60	PODLAHOVÉ KRYTINY UVEDENÉ V TAB. LEGENDA MÍSTNOSTÍ NEJSOU ZAVAZUJÍCÍ A BUDOU INVESTOREM UPŘESNĚNY PŘED ZAPOČETÍM STAVBY. UPOZORŇUJEME, ŽE PODLAHOVÉ KRYTINY JE POTŘEBA VYBÍRAT TAK, ABY BYLY VHODNÉ PRO PODLAHOVÉ VYTÁPĚNÍ.			
UŽITNÁ PLOCHA SO-02:		47,60				
ZASTAVĚNÁ PLOCHA CELKEM:		131,26				

POZNÁMKY:

OKNA S TROJSKLEM, IZOLACE OSTĚNÍ OTVORŮ PROVEDENA V TL. 30 MM

V OBJEKTU RD (KAŽDÉ SO) BUDE UMÍSTĚN PROTIPOŽÁRNÍ HLÁSIČ, HASÍCÍ PŘÍSTROJ S HASÍCÍ SCHOPNOSTÍ MIN. 34A, AUTONOMNÍ DETEKCE A SIGNALIZACE POŽÁRU UMÍSTĚNA V ČÁSTI VEDOUCÍ K VÝCHODU - VIZ POŽÁRNÍ ZPRÁVA (SAMOSTATNÁ PŘÍLOHA PD)

NAD KOUPELNOU BUDE UMÍSTĚN SDK DO VLHKÉHO PROSTŘEDÍ (ZELENÝ)

ÚPRAVA OTVORŮ OBLOŽKOVÝCH ZÁRUBNÍ BUDE UPRAVENA DLE DODAVATELE DVEŘÍ A ZÁRUBNÍ PŘEDPOKLADEM PRO OBLOŽKOVÉ DVEŘE JE OTVOR O 50MM VYŠŠÍ A O 50MM ŠIRŠÍ NA KAŽDOU STRANU

PODLAHOVÉ VYTÁPĚNÍ REALIZOVAT DLE TECHNOLOGICKÝCH PŘEDPISŮ VÝROBCE

PODLAHOVÉ KRYTINY UVEDENÉ V TAB. LEGENDA MÍSTNOSTÍ NEJSOU ZAVAZUJÍCÍ A BUDOU INVESTOREM UPŘESNĚNY PŘED ZAPOČETÍM STAVBY. UPOZORŇUJEME, ŽE PODLAHOVÉ KRYTINY JE POTŘEBA VYBÍRAT TAK, ABY BYLY VHODNÉ PRO PODLAHOVÉ VYTÁPĚNÍ.

V MÍSTĚ OTVORŮ U VNITŘNÍCH DVEŘÍ V PŘÍČKÁCH A V PROSTORU VCHODOVÝCH A FRANCOUZSKÝCH DVEŘÍ NEJSOU UMÍSTĚNY TVÁRNICE!

POD OBVODOVÝMI OTVORY JSOU UMÍSTĚNY NASTAVOVACÍ PRVKY DLE DODAVATELE OKEN - NAPŘ. PURENIT (ELIMINACE TEPELNÉHO MOSTU)

V MÍSTNOSTI 1.03 BUDE UMÍSTĚNA PODLAHOVÁ VPUSŤ SE ZÁPACHOVOU UZÁVĚRKOU I PRO SUCHÝ STAV

PŘEKLADY V PŘÍČKÁCH:
NENOSNÝ PŘEKLAD YTONG NEP 100/125-1250 (1250X249X100/125MM)

PŘEKLADY V OBVODOVÝCH STĚNÁCH:
PŘEKLADY JSOU TVOŘENY SYSTÉMOVÝMI PŘEKLADY NOP A OCELOVÝMI VÁLCOVANÝMI PROFILY

MÍSTNOST 1.03 BUDE ODVĚTRÁNA POMOCÍ EL. VENTILÁTORU V PODHLEDU. VYÚSTĚNÍ EL. VENTILÁTORU V SEVERNÍ ČÁSTI FASÁDY, ZÁROVEŇ VE DVEŘÍCH MÍSTNOSTI BUDE OSAZENA VĚTRACÍ MŘÍŽKA.

KONSTRUKCE JSOU ZAKRESLENY A KÓTOVÁNY BEZ OMÍTEK.
PŘI PROVÁDĚNÍ BUDOU DODRŽENY POŽADAVKY NA MEZNÍ OCHYLKY:
- POVRCHU PODLAH DLE ČSN 74 4505
- VNITŘNÍCH ROVINNÝCH PLOCH DLE ČSN 73 0205
- ORIENTACE KONSTRUKCÍ (PRAVÉ ÚHLY STĚN) DLE ČSN 73 0205

Podepsal Ing. Tomáš Lohr
DN: cn=Ing. Tomáš Lohr, c=CZ, o=Česká komora autorizovaných inženýrů a techniků činných ve výstavbě, ou=0202496, email=lohrtomas@seznam.cz
Datum: 2025.11.03 22:41:10 +01'00'

LEGENDA PODLAH:

m.č. 1.06
- LAMINÁTOVÁ PODLAHA - LAMELY, tl. 10 mm
- MIRELON, tl. 5 mm
- BETONOVÁ MAZANINA, tl. 65 mm+KARI SÍŤ (event. vláknobeton či drátkobeton)
- TEPLOVODNÍ VYTÁPĚNÍ, SYSTÉMOVÁ DESKA REHAU VARIONOVA, tl. 20 mm
- PE FÓLIE
- TEPELNÁ IZOLACE - PODLAHOVÝ POLYSTYREN, tl. 150 mm
- HYDROIZOLACE - 2x SBS MODIFIKOVANÝ ASFALTOVÝ PÁS + PENETRACE

m.č. 1.01, 1.02, 1.03, 1.04, 1.05
- KERAMICKÁ DLAŽBA, tl. 10 mm
- LEPIDLO, tl. 5 mm
- BETONOVÁ MAZANINA, tl. 65 mm + KARI SÍŤ (event. vláknobeton či drátkobeton)
- TEPLOVODNÍ VYTÁPĚNÍ, SYSTÉMOVÁ DESKA REHAU VARIONOVA, tl. 20 mm
- PE FÓLIE
- TEPELNÁ IZOLACE - PODLAHOVÝ POLYSTYREN, tl. 150 mm
- HYDROIZOLACE - 2x SBS MODIFIKOVANÝ ASFALTOVÝ PÁS + PENETRACE

PŮDORYS 1.NP M 1:50

POZN.: VEŠKERÉ KONSTRUKCE PROVÁDĚT DLE TECHNOLOGICKÝCH DOPORUČENÍ VÝROBCE A PŘÍSLUŠNÝCH NOREM
± 0,000 = 327,600 m n.m. Souřadnicový systém JTSK, Výškový systém B.p.v.

Vypracoval: Ing. Tomáš Lohr		Adresa: Klatovská třída 1460/83, 301 00 Plzeň	
Odpovědný projektant: Ing. Tomáš Lohr			
Místo: č.p. 606/2; Obec: Město Touškov [559211] Katastrální území: Město Touškov [693430]			
Investor: Ostreto s.r.o., Denisovo nábřeží 2568/6, Východní Předměstí, 30100 Plzeň	Zakázka:	Měřítko: 1:50	
	Formát: 4xA4	Datum: 09/2025	
Akce: Novostavba řadového rodinného domu - dvojdům	Stupeň: DSP	Paré:	
Obsah: PŮDORYS 1.NP	Č. výkresu: 2		