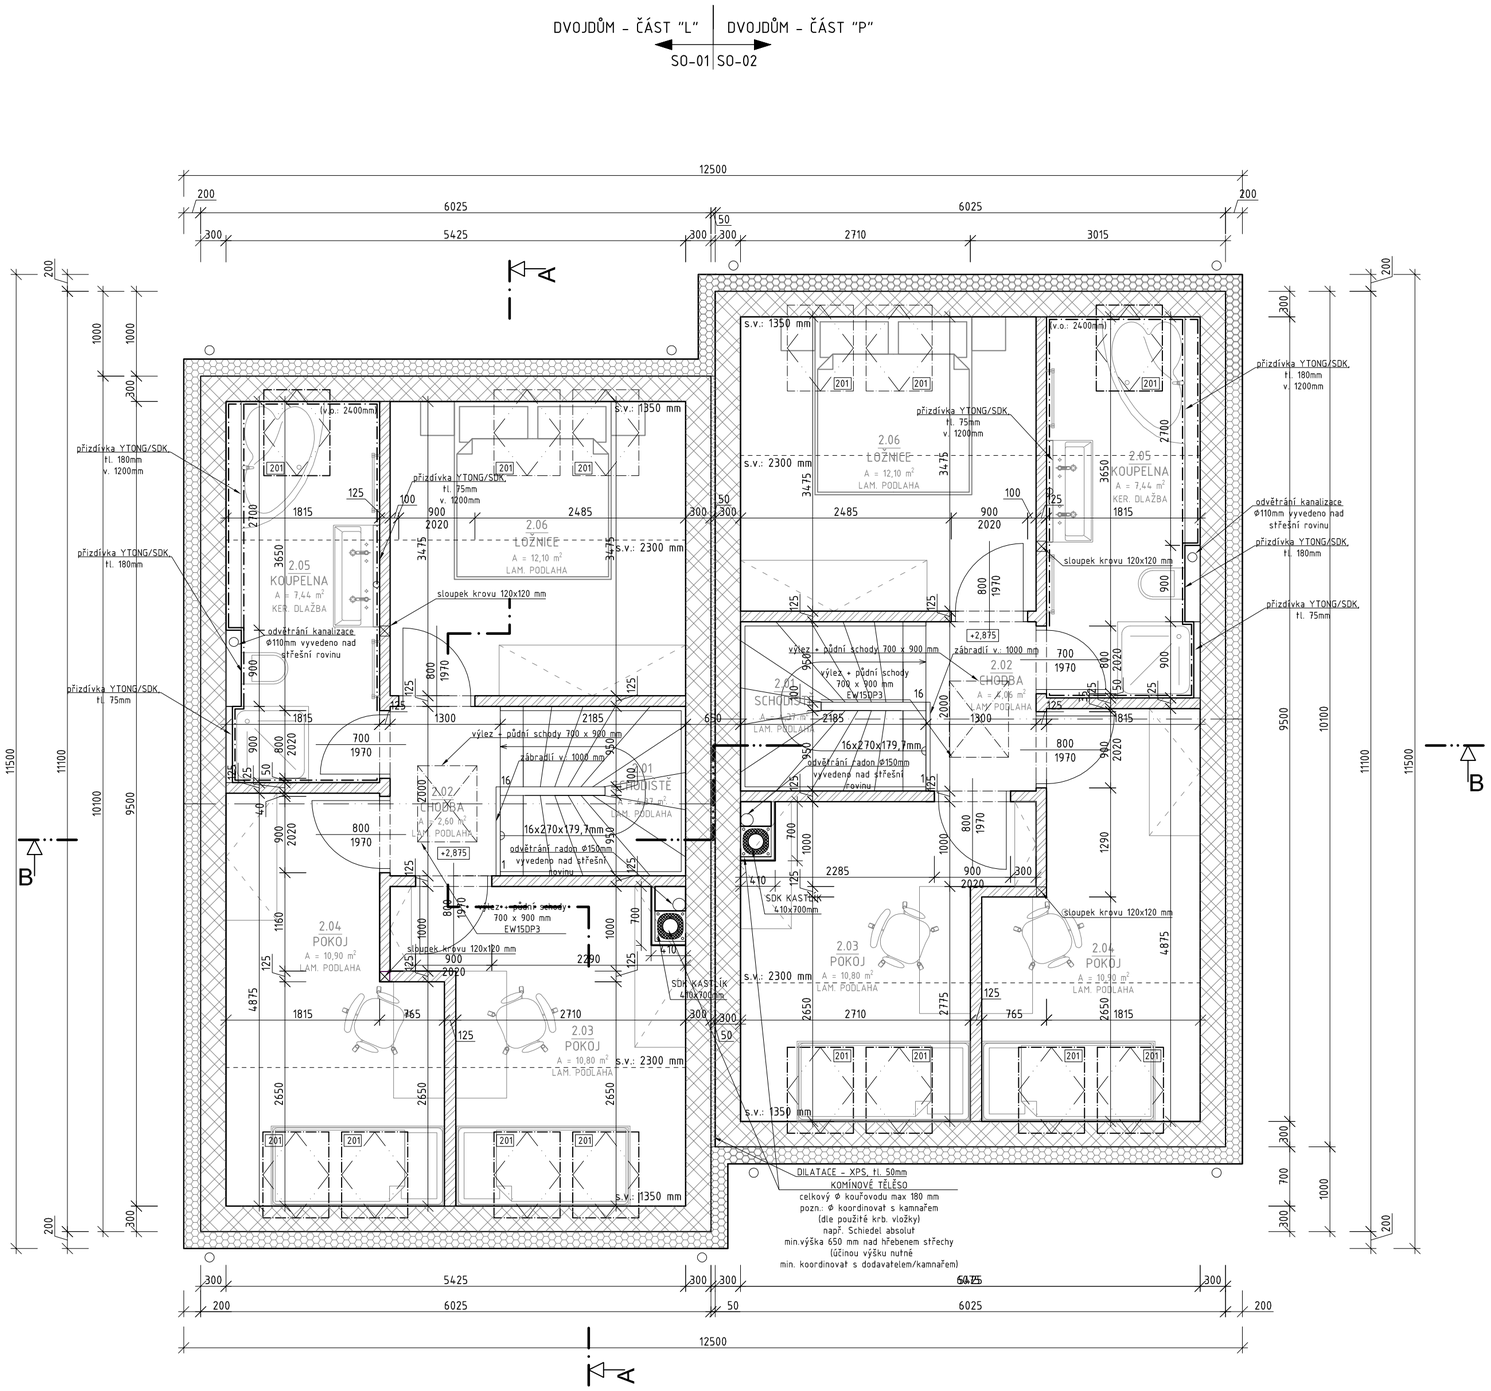


LEGENDA MATERIÁLŮ:

- ZDIVO YTONG STATIK P4-550 PDK, tł. 300 mm (499x300x249mm), NA YTONG TENKOVRSTVÉ MALTOVÉ LOŽE + POLYSTYREN EPS 70 F, tł. 200 mm
- ZDIVO YTONG, tł. 125 mm (599x249x125mm), NA YTONG TENKOVRSTVÉ LEPIDLO
- ZDIVO YTONG, tł. 100 mm (599x249x100mm), NA YTONG TENKOVRSTVÉ LEPIDLO
- INSTALAČNÍ PŘIZDÍVKA, YTONG/SDK, tł. 75–180mm

LEGENDA MÍSTNOSTÍ:

HLAVNÍ OBJEKT – RODINNÝ DŮM:						
č.m.	Účel místnosti	Plocha [m²]	Povrchová úprava			Poznámka
			Podlaha	Stěny	Strop	
2.01	SCHODIŠTĚ	4,37	Laminátová podlaha	Sádrová omítka, SDK +malba	SDK podhled +malba	s.v.: – mm
2.02	CHODBA	2,60	Laminátová podlaha	Sádrová omítka, SDK +malba	SDK podhled +malba	s.v.: 1,35–2,4 m
2.03	POKOJ	10,80	Laminátová podlaha	Sádrová omítka, SDK +malba	SDK podhled +malba	s.v.: 1,35–2,4 m
2.04	POKOJ	10,90	Laminátová podlaha	Sádrová omítka, SDK +malba	SDK podhled +malba	s.v.: 1,35–2,4 m
2.05	KOUPELNA	7,44	Keramická dlažba	Keramický obklad v. 2400 mm	SDK podhled – zel. +malba	s.v.: 1,35–2,4 m
2.06	LOŽNICE	12,10	Laminátová podlaha	Sádrová omítka, SDK +malba	SDK podhled +malba	s.v.: 1,35–2,4 m
UŽITNÁ PLOCHA SO-01:		48,21	PODLAHOVÉ KRYTINY UVEDENÉ V TAB. LEGENDA MÍSTNOSTÍ NEJSOU ZAVAZUJÍCÍ A BUDOU INVESTOREM UPŘESNĚNY PŘED ZAPOČETÍM STAVBY. UPOZORŇUJEME, ŽE PODLAHOVÉ KRYTINY JE POTŘEBA VYBÍRAT TAK, ABY BYLY VHODNÉ PRO PODLAHOVÉ VYTÁPĚNÍ.			
UŽITNÁ PLOCHA SO-02:		48,21				
ZASTAVĚNÁ PLOCHA CELKEM:		131,26				

POZNÁMKY:

OKNA S TROJSKLEM, IZOLACE OSTĚNÍ OTVORŮ PROVEDENA V TL. 30 MM

V OBJEKTU RD BUDE UMÍSTĚN PROTIPOŽÁRNÍ HLÁSIČ, HASÍCÍ PŘÍSTROJ S HASÍCÍ SCHOPNOSTÍ MIN. 34A, AUTONOMNÍ DETEKCE A SIGNALIZACE POŽÁRU UMÍSTĚNA V ČÁSTI VEDOUCÍ K VÝCHODU – VIZ POŽÁRNÍ ZPRÁVA (SAMOSTATNÁ PŘÍLOHA PD)

NAD KOUPELNOU BUDE UMÍSTĚN SDK DO VLHKÉHO PROSTŘEDÍ (ZELENÝ)

ÚPRAVA OTVORŮ OBLOŽKOVÝCH ZÁRUBNÍ BUDE UPRAVENA DLE DODAVATELE DVEŘÍ A ZÁRUBNÍ PŘEDPOKLADEM PRO OBLOŽKOVÉ DVEŘE JE OTVOR O 50MM VYŠŠÍ A O 50MM ŠIRŠÍ NA KAŽDOU STRANU

PODLAHOVÉ VYTÁPĚNÍ REALIZOVAT DLE TECHNOLOGICKÝCH PŘEDPISŮ VÝROBCE

PODLAHOVÉ KRYTINY UVEDENÉ V TAB. LEGENDA MÍSTNOSTÍ NEJSOU ZAVAZUJÍCÍ A BUDOU INVESTOREM UPŘESNĚNY PŘED ZAPOČETÍM STAVBY. UPOZORŇUJEME, ŽE PODLAHOVÉ KRYTINY JE POTŘEBA VYBÍRAT TAK, ABY BYLY VHODNÉ PRO PODLAHOVÉ VYTÁPĚNÍ.

V MÍSTĚ OTVORŮ U VNITŘNÍCH DVEŘÍ V PŘÍČKÁCH A V PROSTORU VCHODOVÝCH A FRANCOUZSKÝCH DVEŘÍ NEJSOU UMÍSTĚNY TVÁRNICE!

POD OBVODOVÝMI OTVORY JSOU UMÍSTĚNY NASTAVOVACÍ PRVKY DLE DODAVATELE OKEN – NAPŘ. PURENIT (ELIMINACE TEPELNÉHO MOSTU)

STŘEŠNÍ OKNA NAPŘ. VELUX 780x1180 mm

PŘEKLADY V PŘÍČKÁCH:
NENOSNÝ PŘEKLAD YTONG NEP 100/125-1250 (1250X249X100/125MM)

PŘEKLADY V OBVODOVÝCH STĚNÁCH:
PŘEKLADY JSOU TVOŘENY SYSTÉMOVÝMI PŘEKLADY NOP A OCELOVÝMI VÁLCOVANÝMI PROFILY

KONSTRUKCE JSOU ZAKRESLENY A KÓTOVÁNY BEZ OMÍTEK.
PŘI PROVÁDĚNÍ BUDOU DODRŽENY POŽADAVKY NA MEZNÍ OCHYLKY:
- POVRCHU PODLAH DLE ČSN 74 4505
- VNITŘNÍCH ROVINNÝCH PLOCH DLE ČSN 73 0205
- ORIENTACE KONSTRUKCÍ (PRAVÉ ÚHLY STĚN) DLE ČSN 73 0205

LEGENDA PODLAH:

m.č. 2.02, 2.03, 2.04, 2.05, 2.07
- LAMINÁTOVÁ PODLAHA – LAMELY, tł. 10 mm
- MIRELON, tł. 5 mm
- BETONOVÁ MAZANINA, tł. 50 mm + KARI SÍŤ (event. vláknobeton či drátkobeton)
- PE FÓLIE
- TEPELNÁ IZOLACE – PODLAHOVÝ POLYSTYREN, tł. 40 mm
- KROČEJOVÁ PODLAHOVÁ IZOLACE, tł. 20 mm
- STROPNÍ KONSTRUKCE LIABET, tł. 250 mm

m.č. 2.06
- KERAMICKÁ DLAŽBA, tł. 10 mm
- LEPIDLO, tł. 5 mm
- (navíc v m.č. 2.06): 2x HI stěrka 1–1,5 mm, vytažena cca 150 mm na stěnu a do výšky 2,4 m kolem vany a sprchového koutu
- BETONOVÁ MAZANINA, tł. 50 mm + KARI SÍŤ (event. vláknobeton či drátkobeton)
- PE FÓLIE
- TEPELNÁ IZOLACE – PODLAHOVÝ POLYSTYREN, tł. 40 mm
- KROČEJOVÁ PODLAHOVÁ IZOLACE, tł. 20 mm
- STROPNÍ KONSTRUKCE LIABET, tł. 250 mm

PŮDORYS PODKROVÍ M 1:50

Podepsal Ing. Tomáš Lohr
DN: cn=Ing. Tomáš Lohr, c=CZ, o=Česká komora autorizovaných inženýrů a techniků činných ve výstavbě, ou=0202496, email=lohrtomas@seznam.cz
Datum: 2025.11.03 22:42:43 +01'00'

POZN.: VEŠKERÉ KONSTRUKCE PROVÁDĚT DLE TECHNOLOGICKÝCH DOPORUČENÍ VÝROBCE A PŘÍSLUŠNÝCH NOREM
± 0,000 = 327,600 m n.m. Souřadnicový systém JTSK, Výškový systém B.p.v.

Vypracoval: Ing. Tomáš Lohr		Adresa: Klatovská třída 1460/83, 301 00 Plzeň	
Odpovědný projektant: Ing. Tomáš Lohr			
Místo: č.p. 606/2; Obec: Město Touškov [559211] Katastrální území: Město Touškov [693430]			
Investor: Ostreto s.r.o., Denisovo nábřeží 2568/6, Východní Předměstí, 30100 Plzeň	Zakázka:	Měřítko: 1:50	
	Formát: 4xA4	Datum: 09/2025	
Akce: Novostavba řadového rodinného domu – dvojdům	Stupeň: DSP	Paré:	
Obsah: PŮDORYS PODKROVÍ	Č. výkresu: 4		