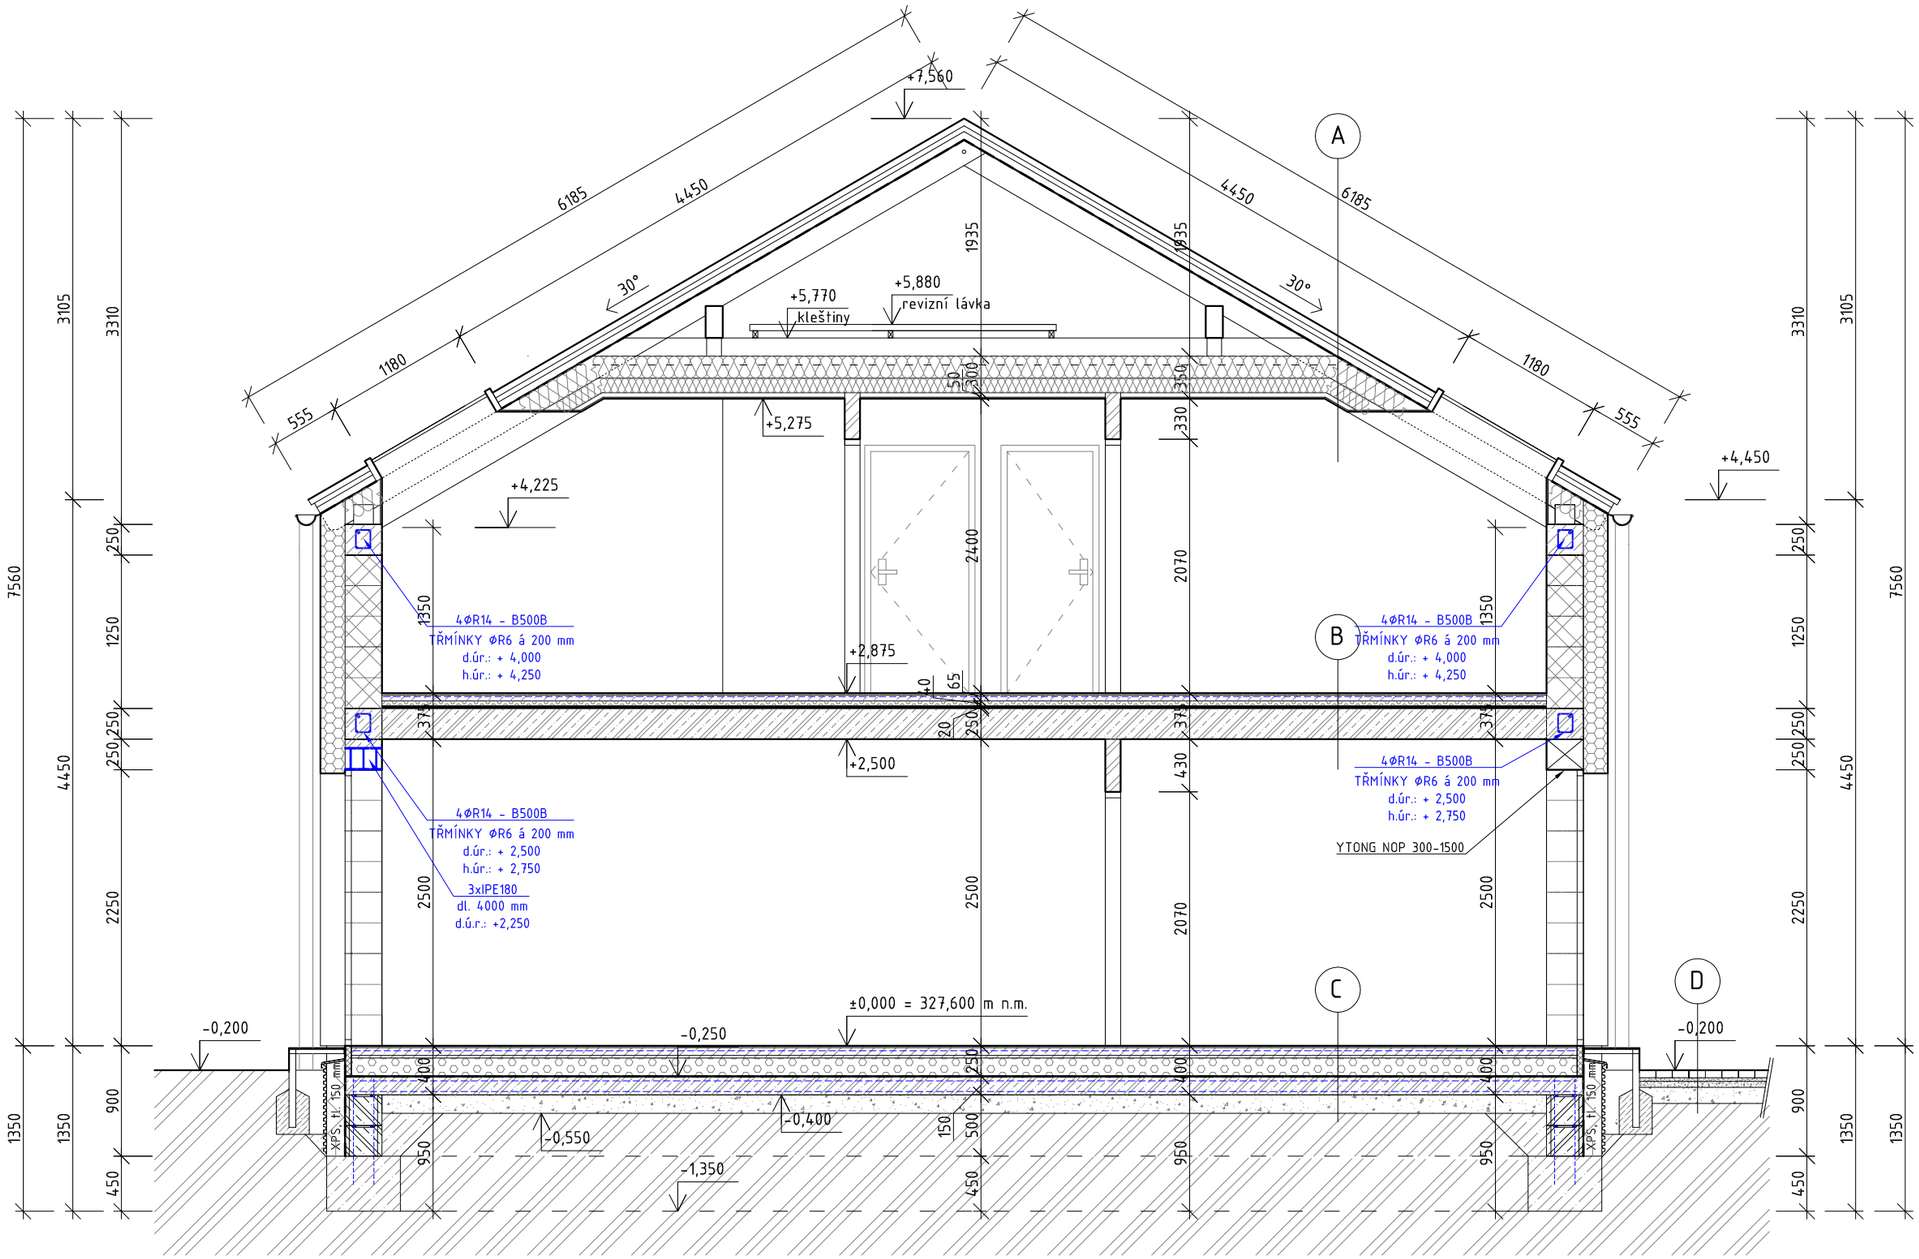


SKLADBY KONSTRUKCÍ:

SKLADBA - A
- STŘEŠNÍ KRYTINA BRAMAC - barva dle výběru investora
- STŘEŠNÍ LATĚ 40/60mm - VZDÁLENOST DLE TAŠEK
- KONTRALATĚ 60/40mm - provětrávaná mezera min 60mm nasávání u okapu, odvětrání u hřebene střechy
- POJISTNÁ HYDROIZOLAČNÍ FOLIE (DIFUZNĚ PROPUSTNÁ) dle doporučení výrobce
- KROKVE 100/180 mm + izolace mezi krokvemi Isover Unirol Profi, tl. 180 mm
- TEPELNÁ IZOLACE, Isover Unirol Profi, tl. 120mm
- PAROZÁBRANA např. DELTA REFLEX (alt. JUTAFOL N, GUTAFOL WB)
- SÁDROKARTONOVÝ PODHLED
- SÁDROKARTON tl: 12,5mm - REI15/DP3
(do vlhkých prostor použít SDK k tomu určené - zelená barva)
VE STŘEŠNÍM PLÁŠTI NAD KOUPELNOU MUSÍ BÝT PAROZÁBRANA UMÍSTĚNA TĚSNĚ NAD SÁDROKARTONOVÝMI DESKAMI (VE SMĚRU Z INTERIÉRU) A ŘÁDNĚ UTĚSNĚNA

SKLADBA - B
- NÁŠLAPNÁ VRSTVA PODLAHY - DLE VOLBY INVESTORA tl. 15.mm
- BETONOVÁ MAZANINA tl. 50mm + KARI SÍŤ U HORNÍHO POVRCHU
- PE FÓLIE
- TEPELNÁ IZOLACE - PODLAHOVÝ POLYSTYREN, tl. 40 mm
- KROČEJOVÁ PODLAHOVÁ IZOLACE, tl. 20 mm
- STROPNÍ KONSTRUKCE LIABET, tl. 250 mm

SKLADBA - C
- NÁŠLAPNÁ VRSTVA PODLAHY - DLE VOLBY INVESTORA tl. 15.mm
- BETONOVÁ MAZANINA tl. 65mm + KARI SÍŤ U HORNÍHO POVRCHU
- TEPLOVODNÍ VYTÁPĚNÍ, SYSTÉMOVÁ DESKA REHAU VARIONOVA, tl. 20 mm
- PE FÓLIE
- TEPELNÁ IZOLACE - PODLAHOVÝ POLYSTYREN, tl. 150 mm
- HYDROIZOLACE - 2 x SBS modifikovaný asfaltový pás + penetrace
- ZÁKLADOVÁ DESKA C20/25 tl. 150 mm S KARI SÍTÍ 2 x 150/150x8 (event. 100/100x6)
- ŠTĚRKOVÝ PODSYP tl. 150 mm
- PŮVODNÍ ZEMINA

SKLADBA D - zpevněná plocha
(dle doporučení dodavatele dlažby)
- ZÁMKOVÁ DLAŽBA, tl. 60 mm
- KLADECÍ VRSTVA, kamenivo frakce 4-8 mm, tl. 30 mm
- DRCENÉ KAMENIVO fr. 8 -16 mm, tl. 50 mm
- DRCENÉ KAMENIVO fr. 0 - 63mm, tl. 200 mm
- PŮVODNÍ ZEMINA

Podepsal Ing. Tomáš Lohr
DN: cn=Ing. Tomáš Lohr, c=CZ, o=Česká komora autorizovaných inženýrů a techniků činných ve výstavbě, ou=0202496, email=lohrtomas@seznam.cz
Datum: 2025.11.03 22:42:51 +01'00'

LEGENDA MATERIÁLŮ:

- ZDIVO YTONG STATIK P4-550 PDK, tl. 300 mm (499x300x249mm), NA YTONG TENKOVRSTVÉ MALTOVÉ LOŽE + POLYSTYREN EPS 70 F, tl. 200 mm
- ZDIVO YTONG, tl. 125 mm (599x249x125mm), NA YTONG TENKOVRSTVÉ LEPIDLO
- INSTALAČNÍ PŘIZDÍVKY, DOZDÍVKY, YTONG tl. 75-180 mm
- HYDRO- / PROTIRAD. IZOLACE - 300 mm NAD ÚROVEŇ TERÉNU TĚSNIT VŠECHNY PROSTUPY PROTIRADONOVOU IZOLACÍ
- KARI SÍTĚ, OCEL. VÝZTUŽE
- TEPELNÁ IZOLACE - POLYSTYREN podlahový EPS
- TEPELNÁ IZOLACE - POLYSTYREN fasádní EPS
- TEPELNÁ IZOLACE - POLYSTYREN XPS VE STYKU SE ZEMINOU CHRÁNIT NOPOVOU FÓLÍÍ
- TEPELNÁ IZOLACE - MINERÁLNÍ VATA
- PŮVODNÍ ZEMINA
- BETON
- ŠTĚRKOPÍSKOVÝ PODSYP
- NASYPANÁ ZEMINA - pův. výkopek
- PROPUSTNÝ NÁSYP - oblázky, štěrk
- ŽELEZOBETON

ŘEZ A-A M 1:50

POZN.: VEŠKERÉ KONSTRUKCE PROVÁDĚT DLE TECHNOLOGICKÝCH DOPORUČENÍ VÝROBCE A PŘÍSLUŠNÝCH NOREM

± 0,000 = 327,600 m n.m. Souřadnicový systém JTSK, Výškový systém B.p.v.

Vypracoval: Ing. Tomáš Lohr		Adresa: Klatovská třída 1460/83, 301 00 Plzeň	
Odpovědný projektant: Ing. Tomáš Lohr			
Místo: č.p. 606/2; Obec: Město Touškov [559211] Katastrální území: Město Touškov [693430]			
Investor: Ostreto s.r.o., Denisovo nábřeží 2568/6, Východní Předměstí, 30100 Plzeň		Zakázka:	Měřítko: 1:50
		Formát: 2xA4	Datum: 09/2025
Akce: Novostavba řadového rodinného domu - dvojdům		Stupeň: DSP	Paré:
Obsah: ŘEZ A-A		Č. výkresu: 7	